


給排水衛生設備 平面図

PLUMBING & SANITARY PLAN / 2F

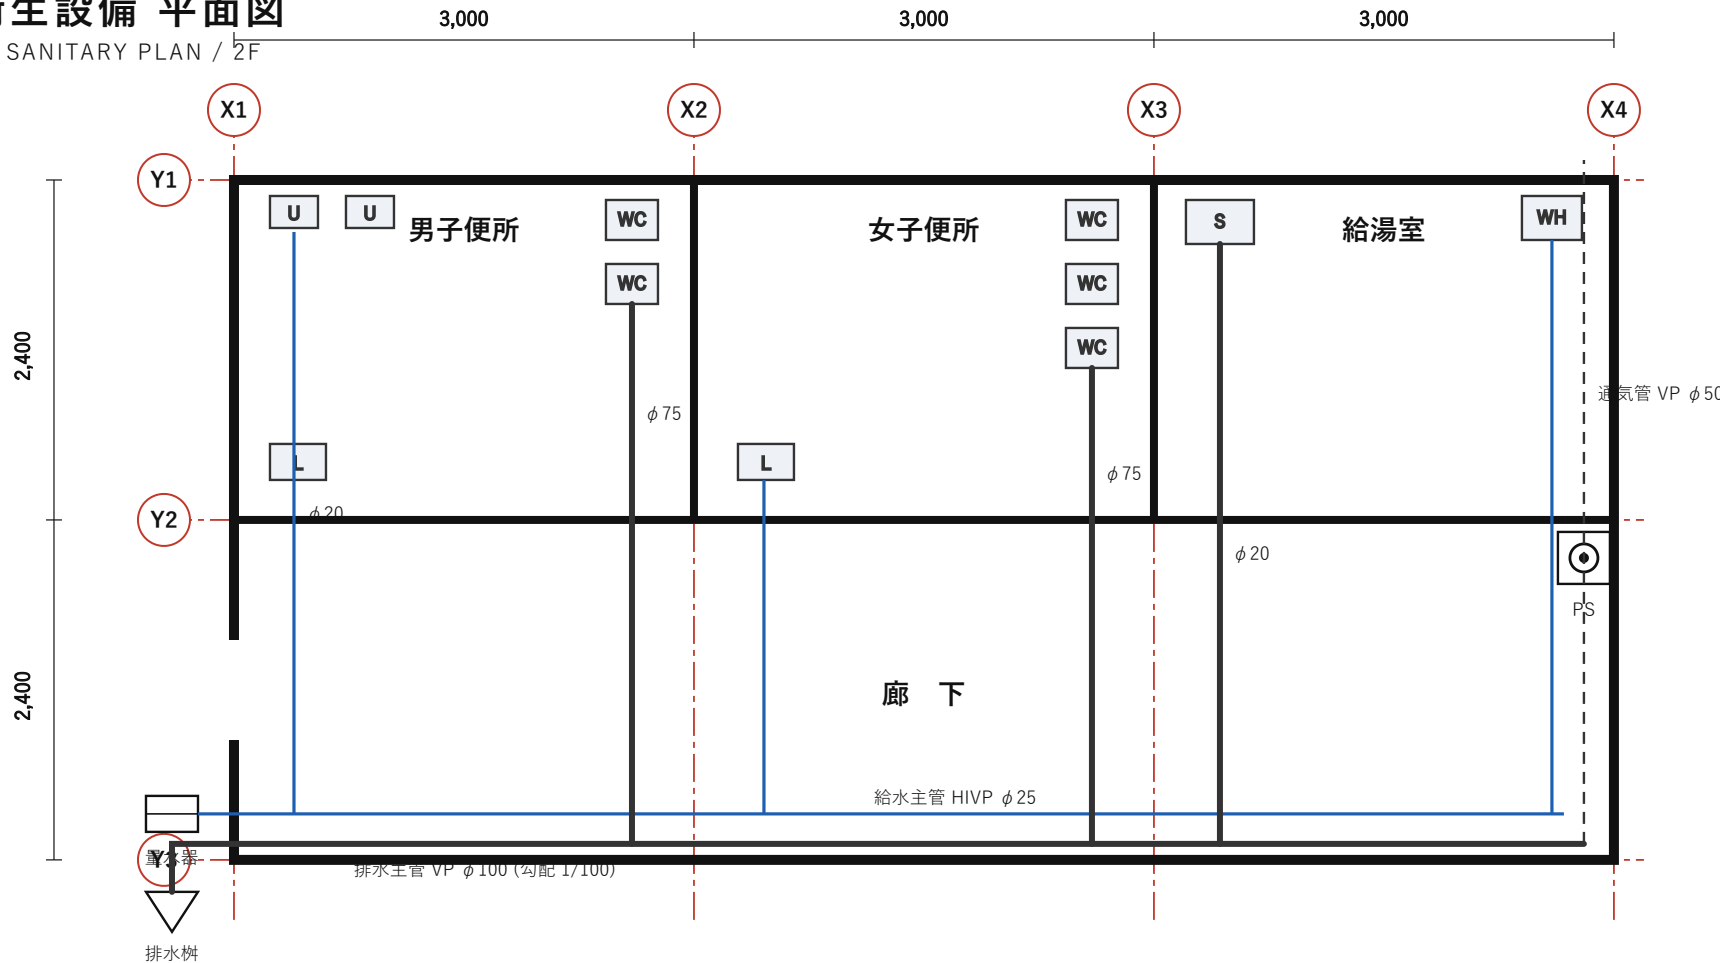

凡例 / LEGEND

WC … 大便器
L … 洗面器
WH … 給湯器
量水器

U … 小便器
S … 流し
PS … 立管
排水樹 (▽)

給水管 (HIVP)
排水管 (VP)
通気管 (VP)

注記 / NOTES

- 本図は2階 給排水衛生設備の平面図を示す。
- 給水管はHIVP、排水管・通気管はVPとする。
- 寸法は特記なき限りmm単位とする。
- 排水横管の勾配は1/100以上を確保すること。
- 器具取付高さ・詳細は別途詳細図による。
- 隠蔽配管は施工前に他業者と取合いを確認する。
- 試験圧力・水圧試験は監督員立会のうえ実施する。

工事名

サンプルビル 新築工事

図面名

2F 給排水衛生設備 平面図
PLUMBING PLAN

縮尺

1 / 50

A1

図面番号

M - 201

日付

2026-06-09

REV. 0

サンプル設備工業株式会社